


Schnitt A-A

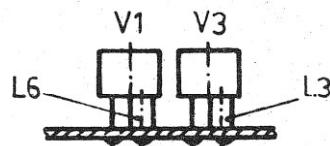

Dargestellt nur V1 u. V3

lichte Höhe unter R5,R7,R8, 6mm


Bauhöhe max. 16,5

Belegungsplan, Helllastverstärker

63-330-3863-0


1.12516952.3/09

36

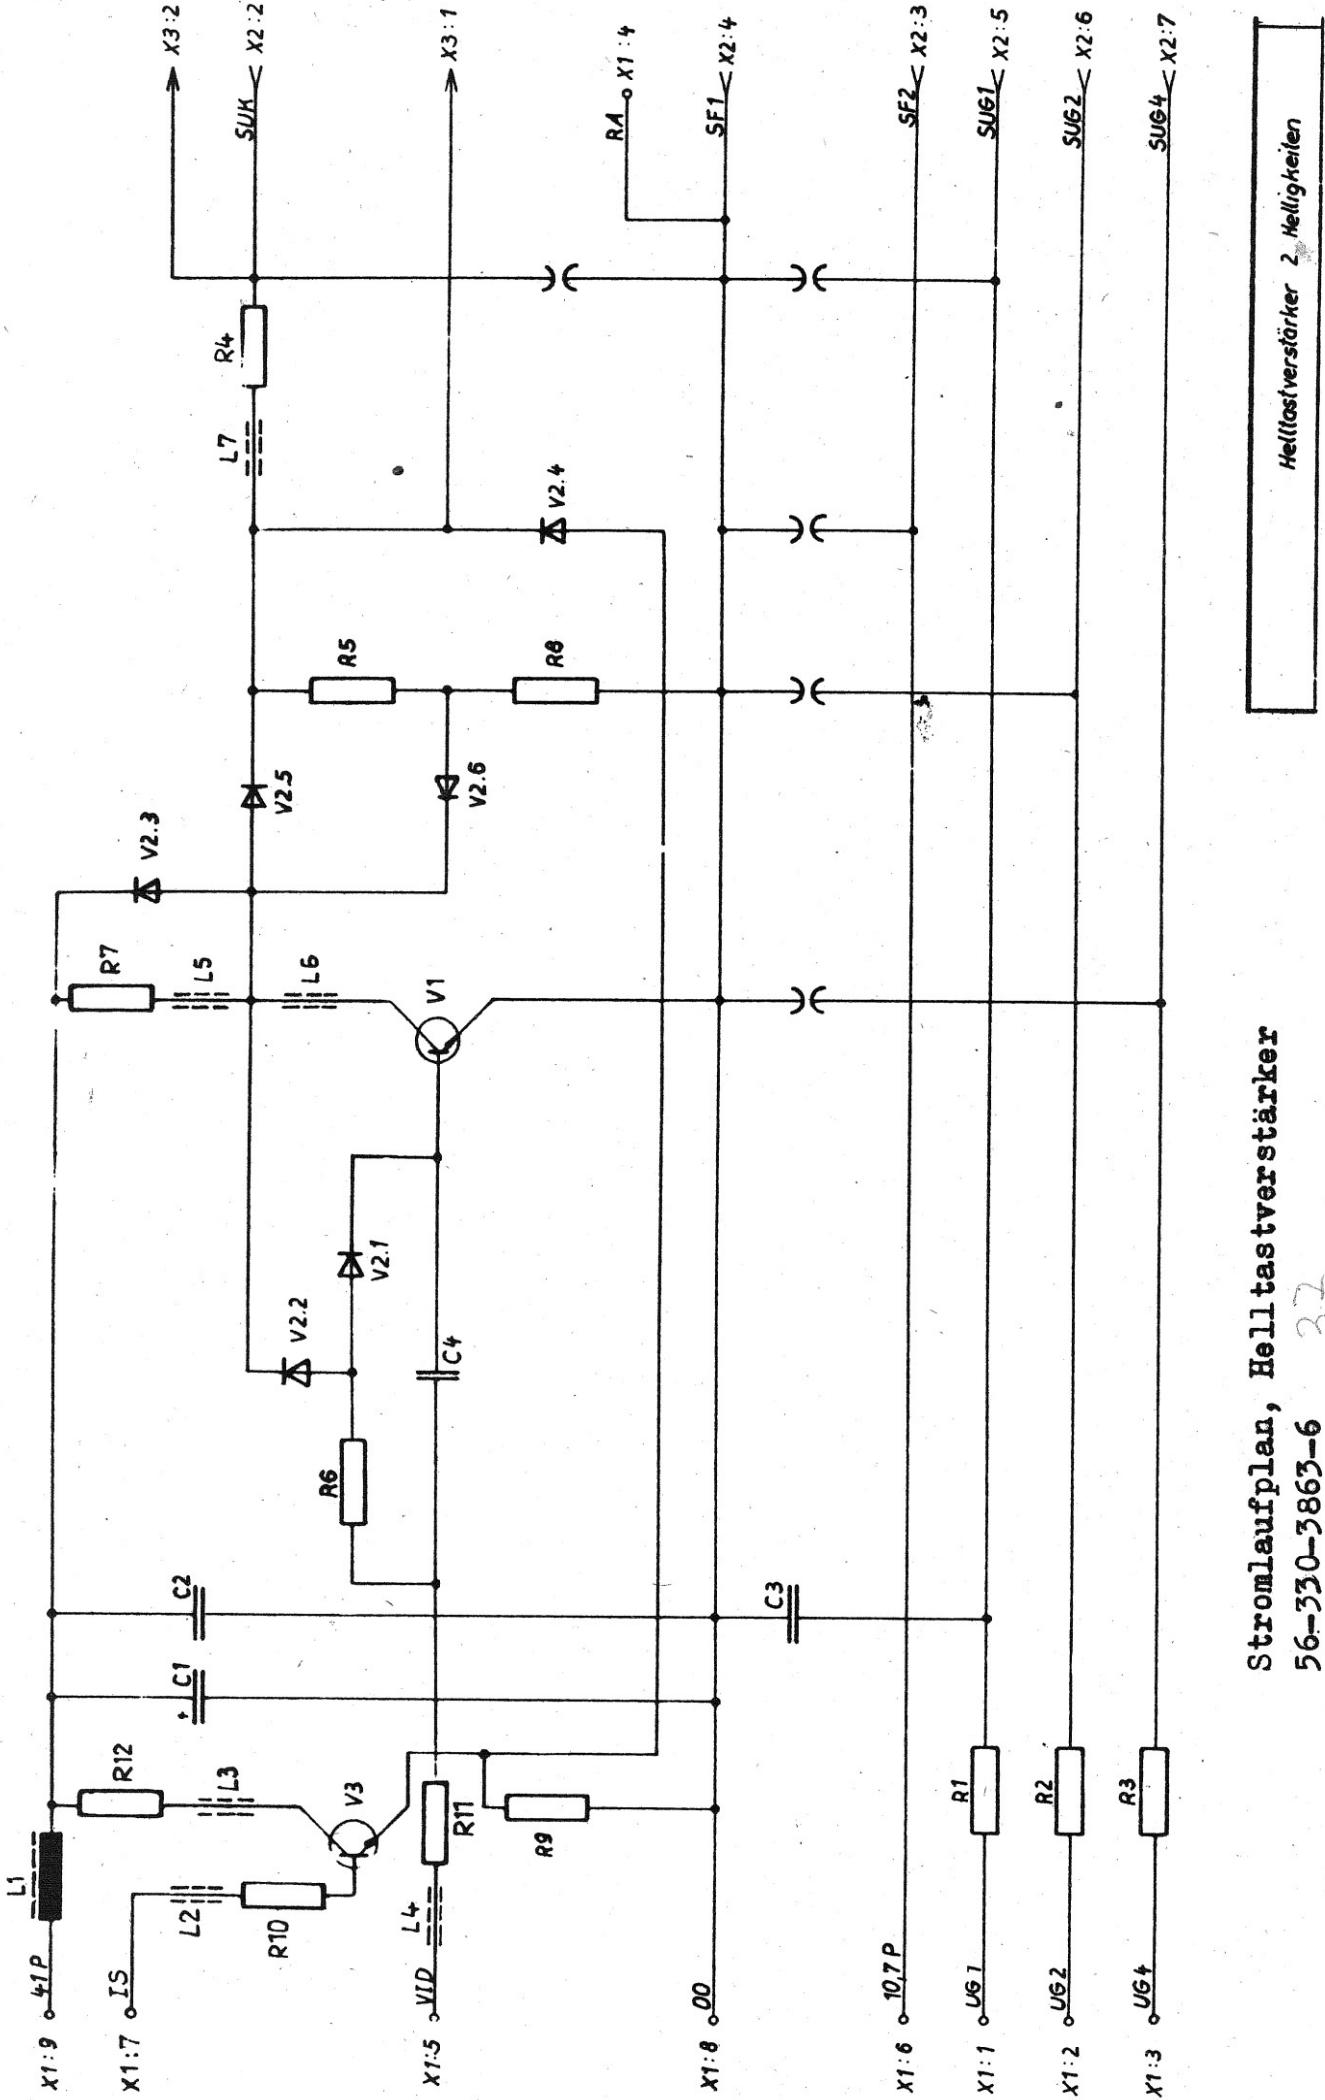


Stromlaufplan, Helltastransistor
 56-330-3863-6 37


Helligkeitsverstärker 2 Helligkeiten

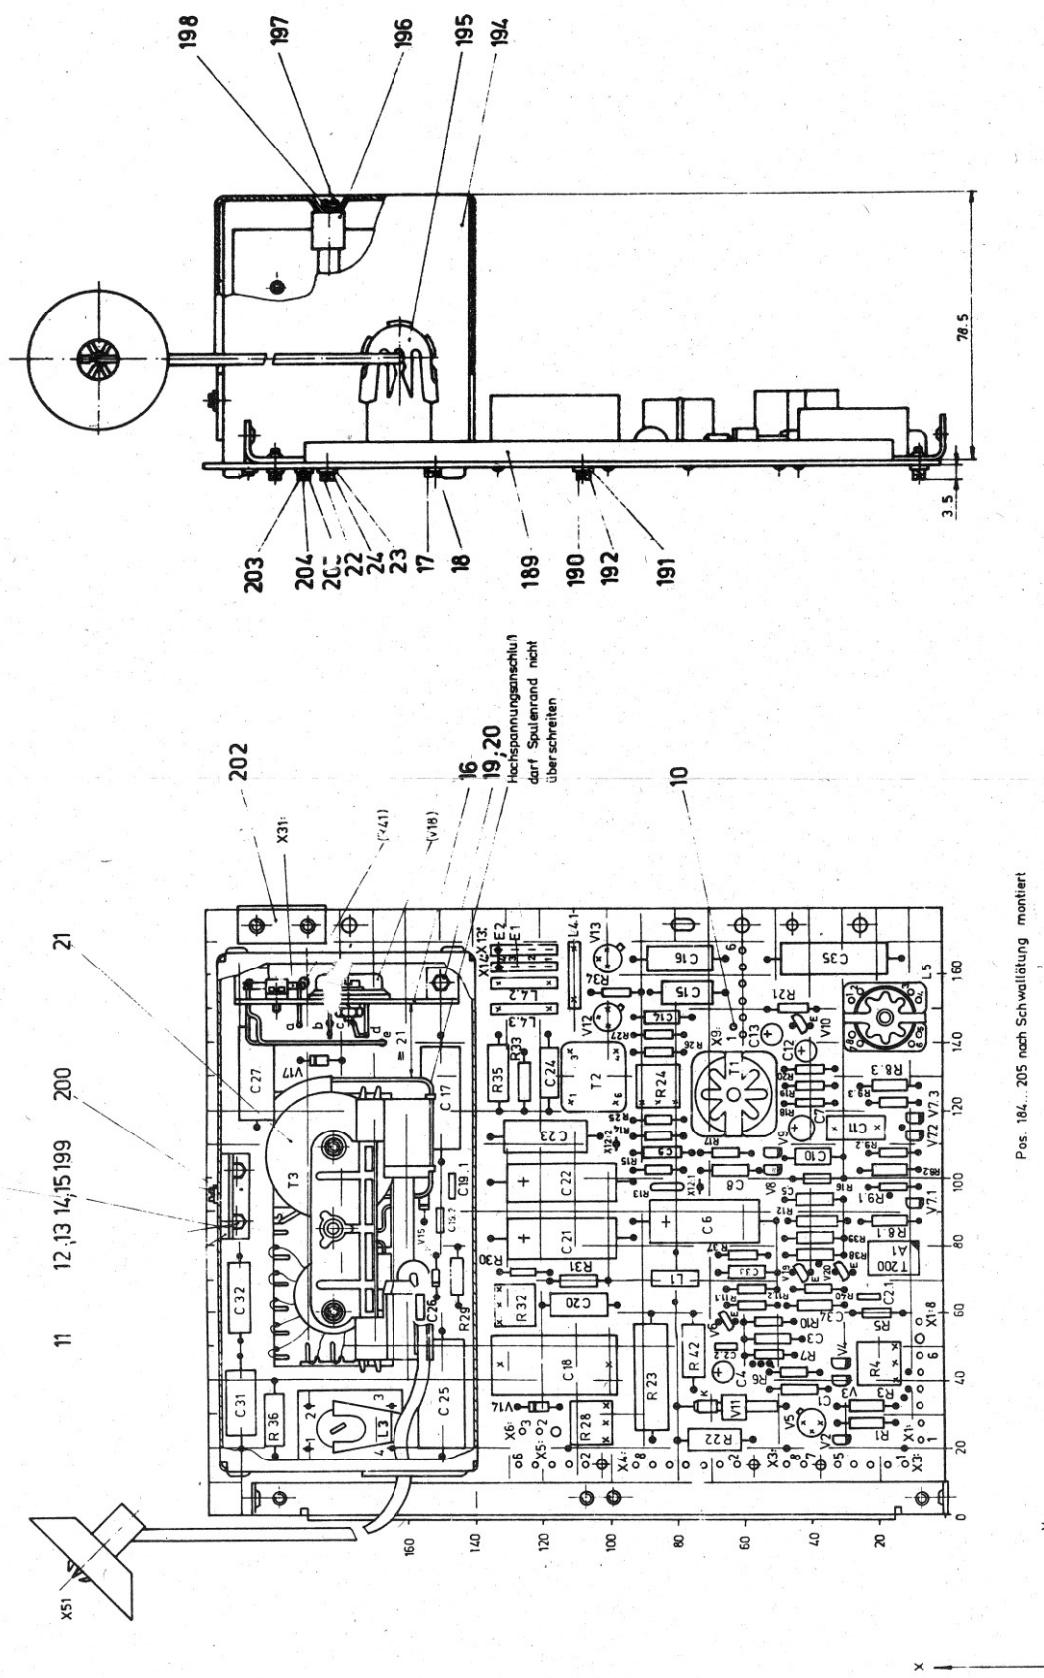

Belegungsplan, Hochspannung
63-330-3860-7
1.12.516922.6/09 38

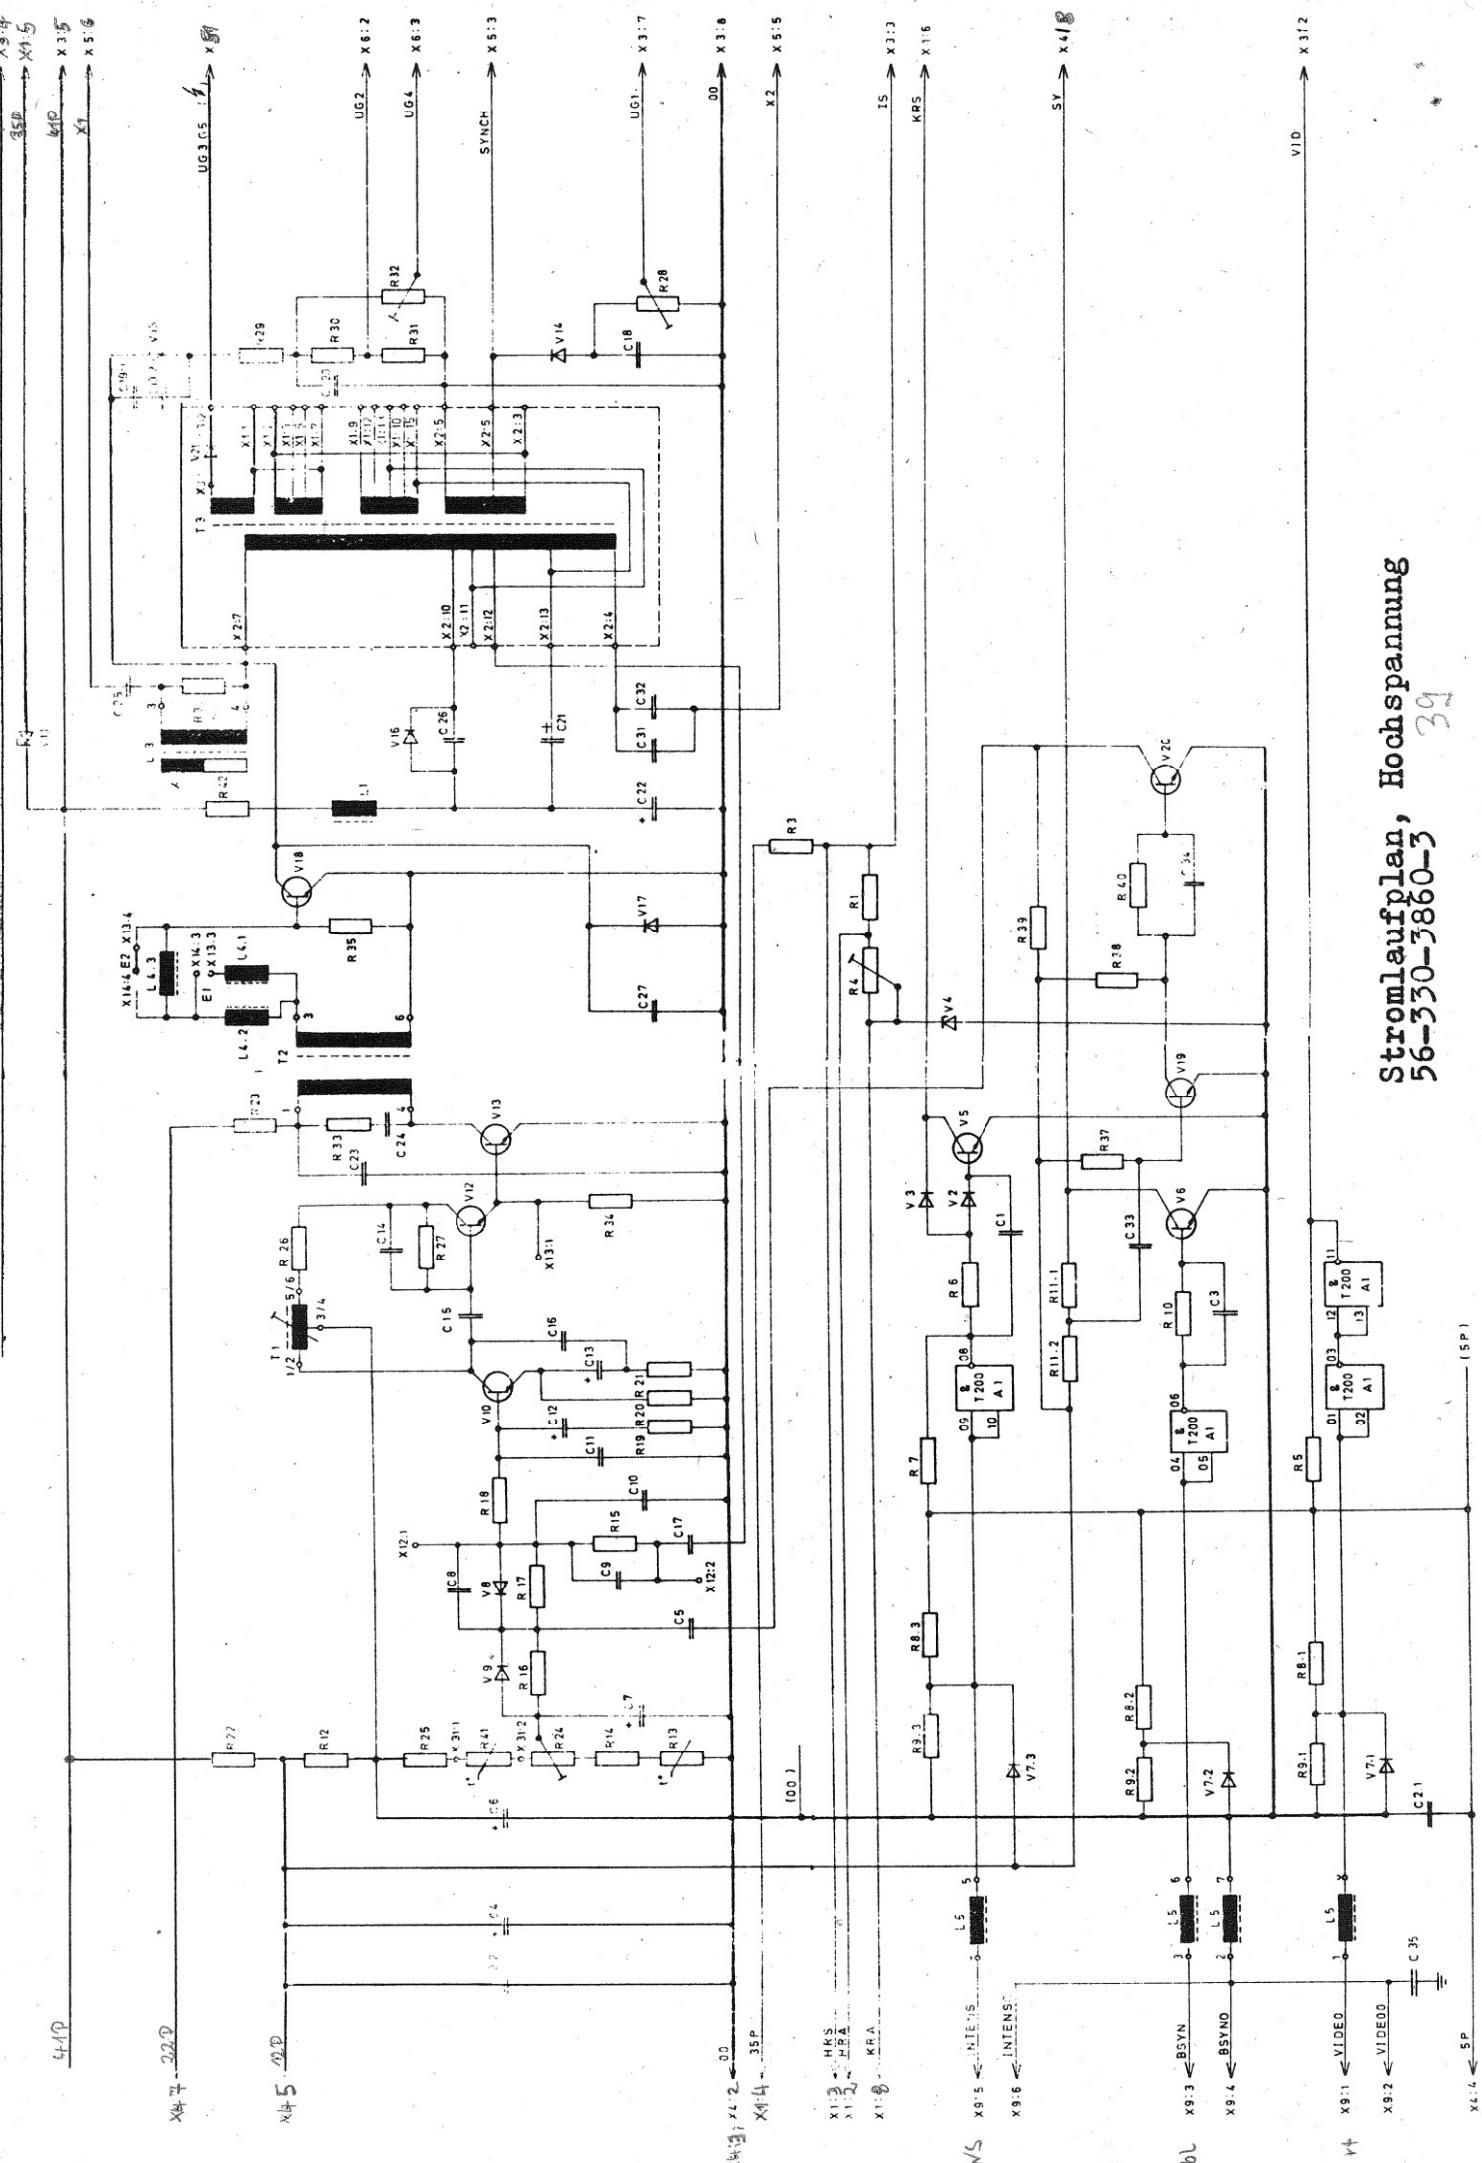


Stromlaufplan, Hochspannung
56-330-3860-3 39

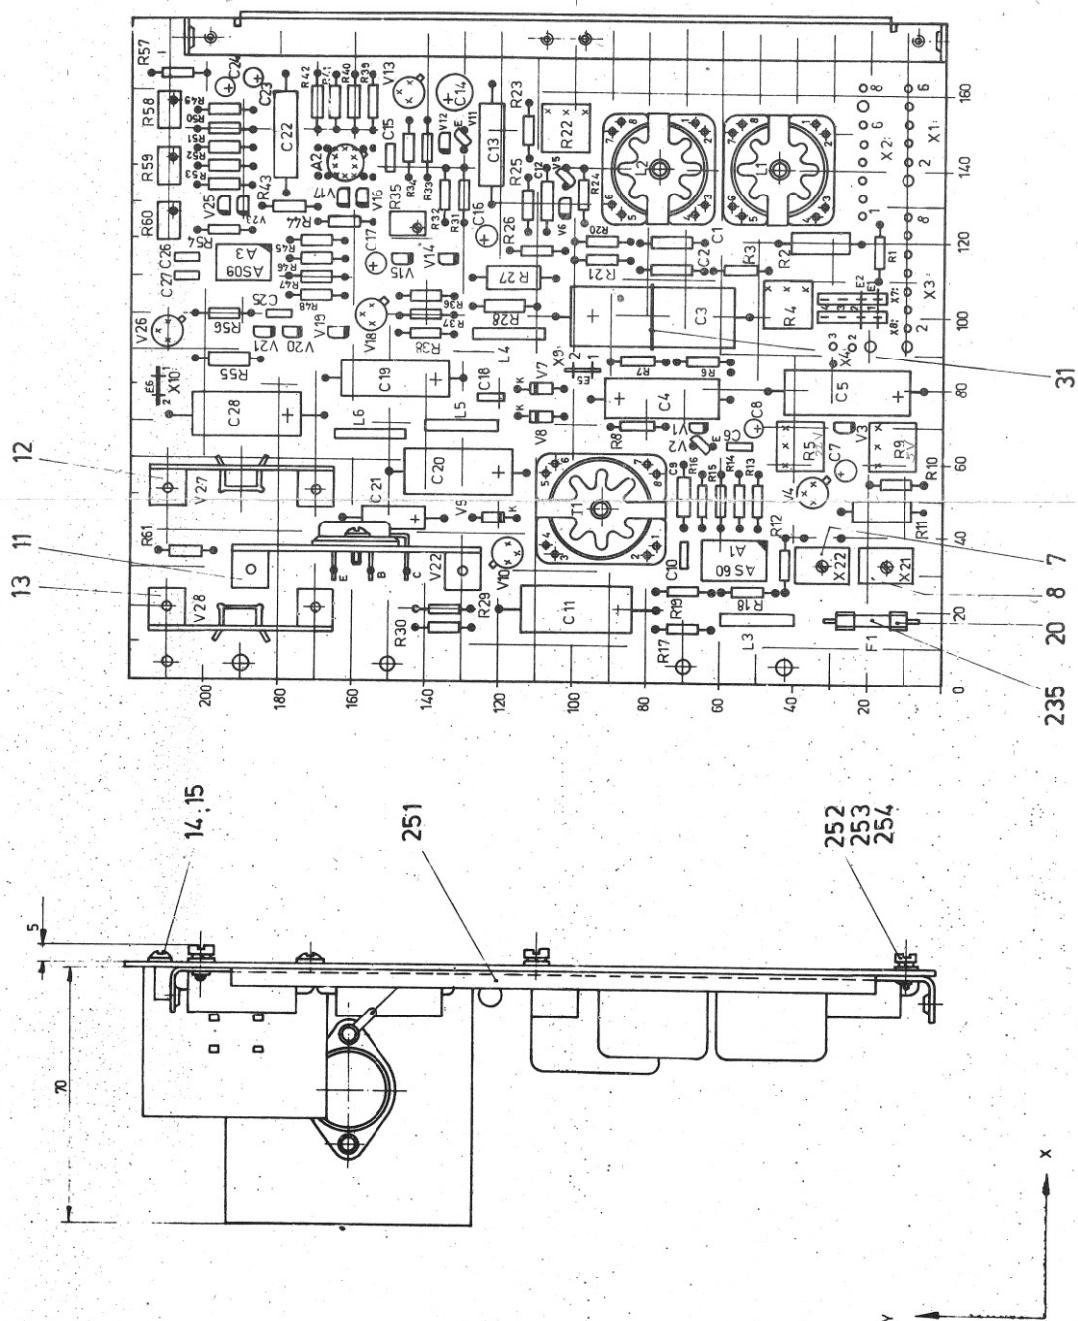



Pos. 231...254 nach Schwallöfen montiert
L3, L6 geklebt mit FimoFix
L - Seite schutzacktiviert

Belegungsplan, Video
63-330-3861-5
1.12.516934.7/09 40


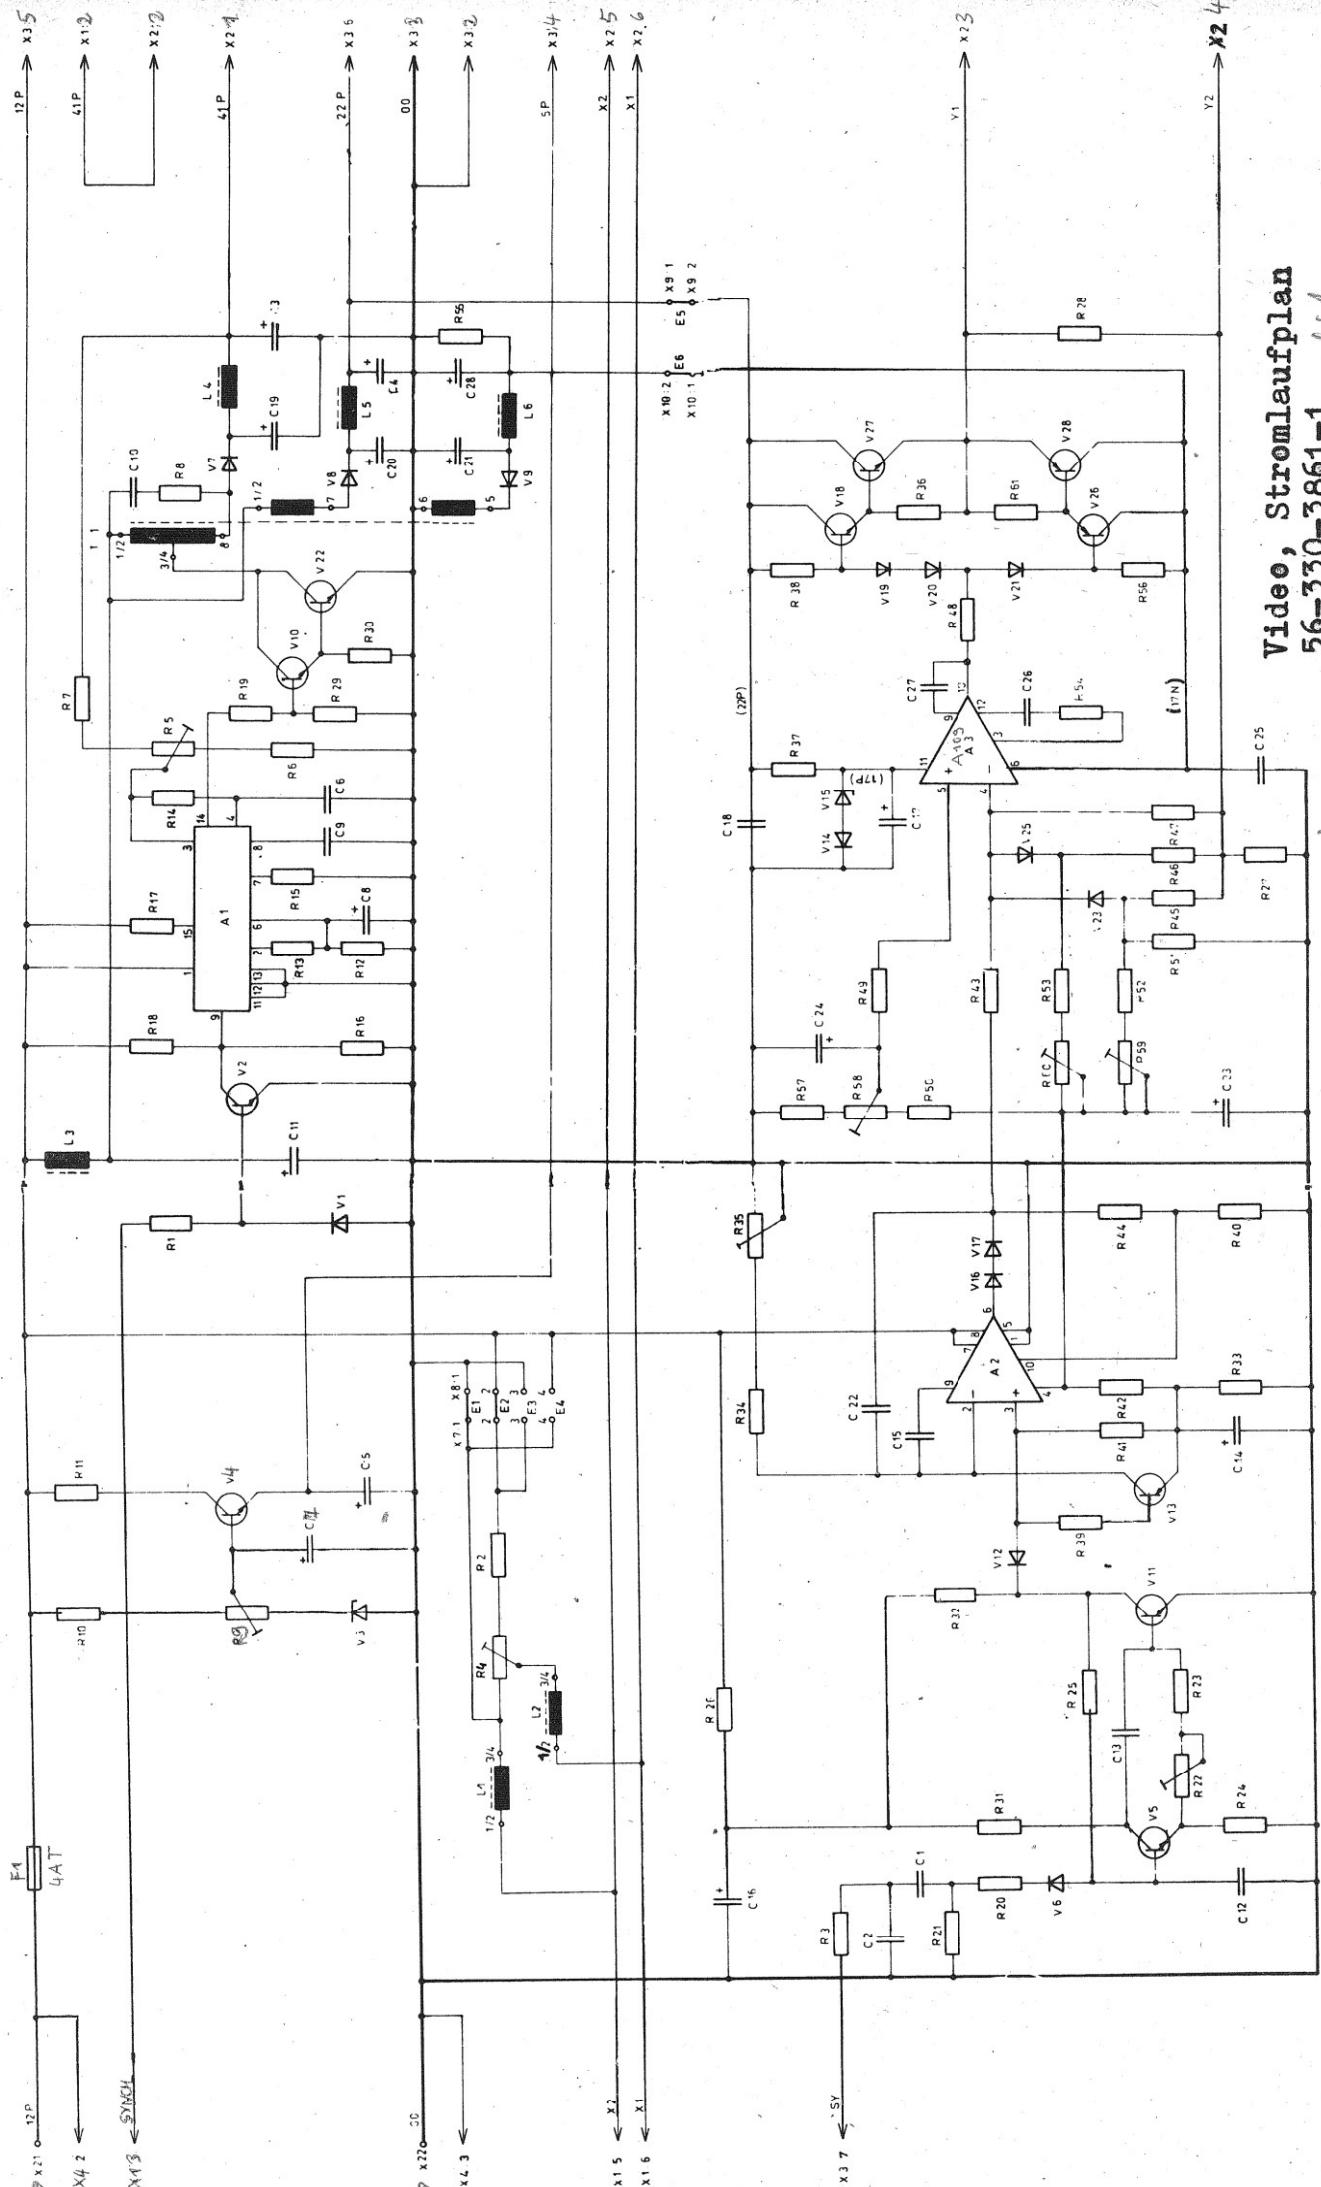


Video, Stromlaufplan
56-330-3861-1 41

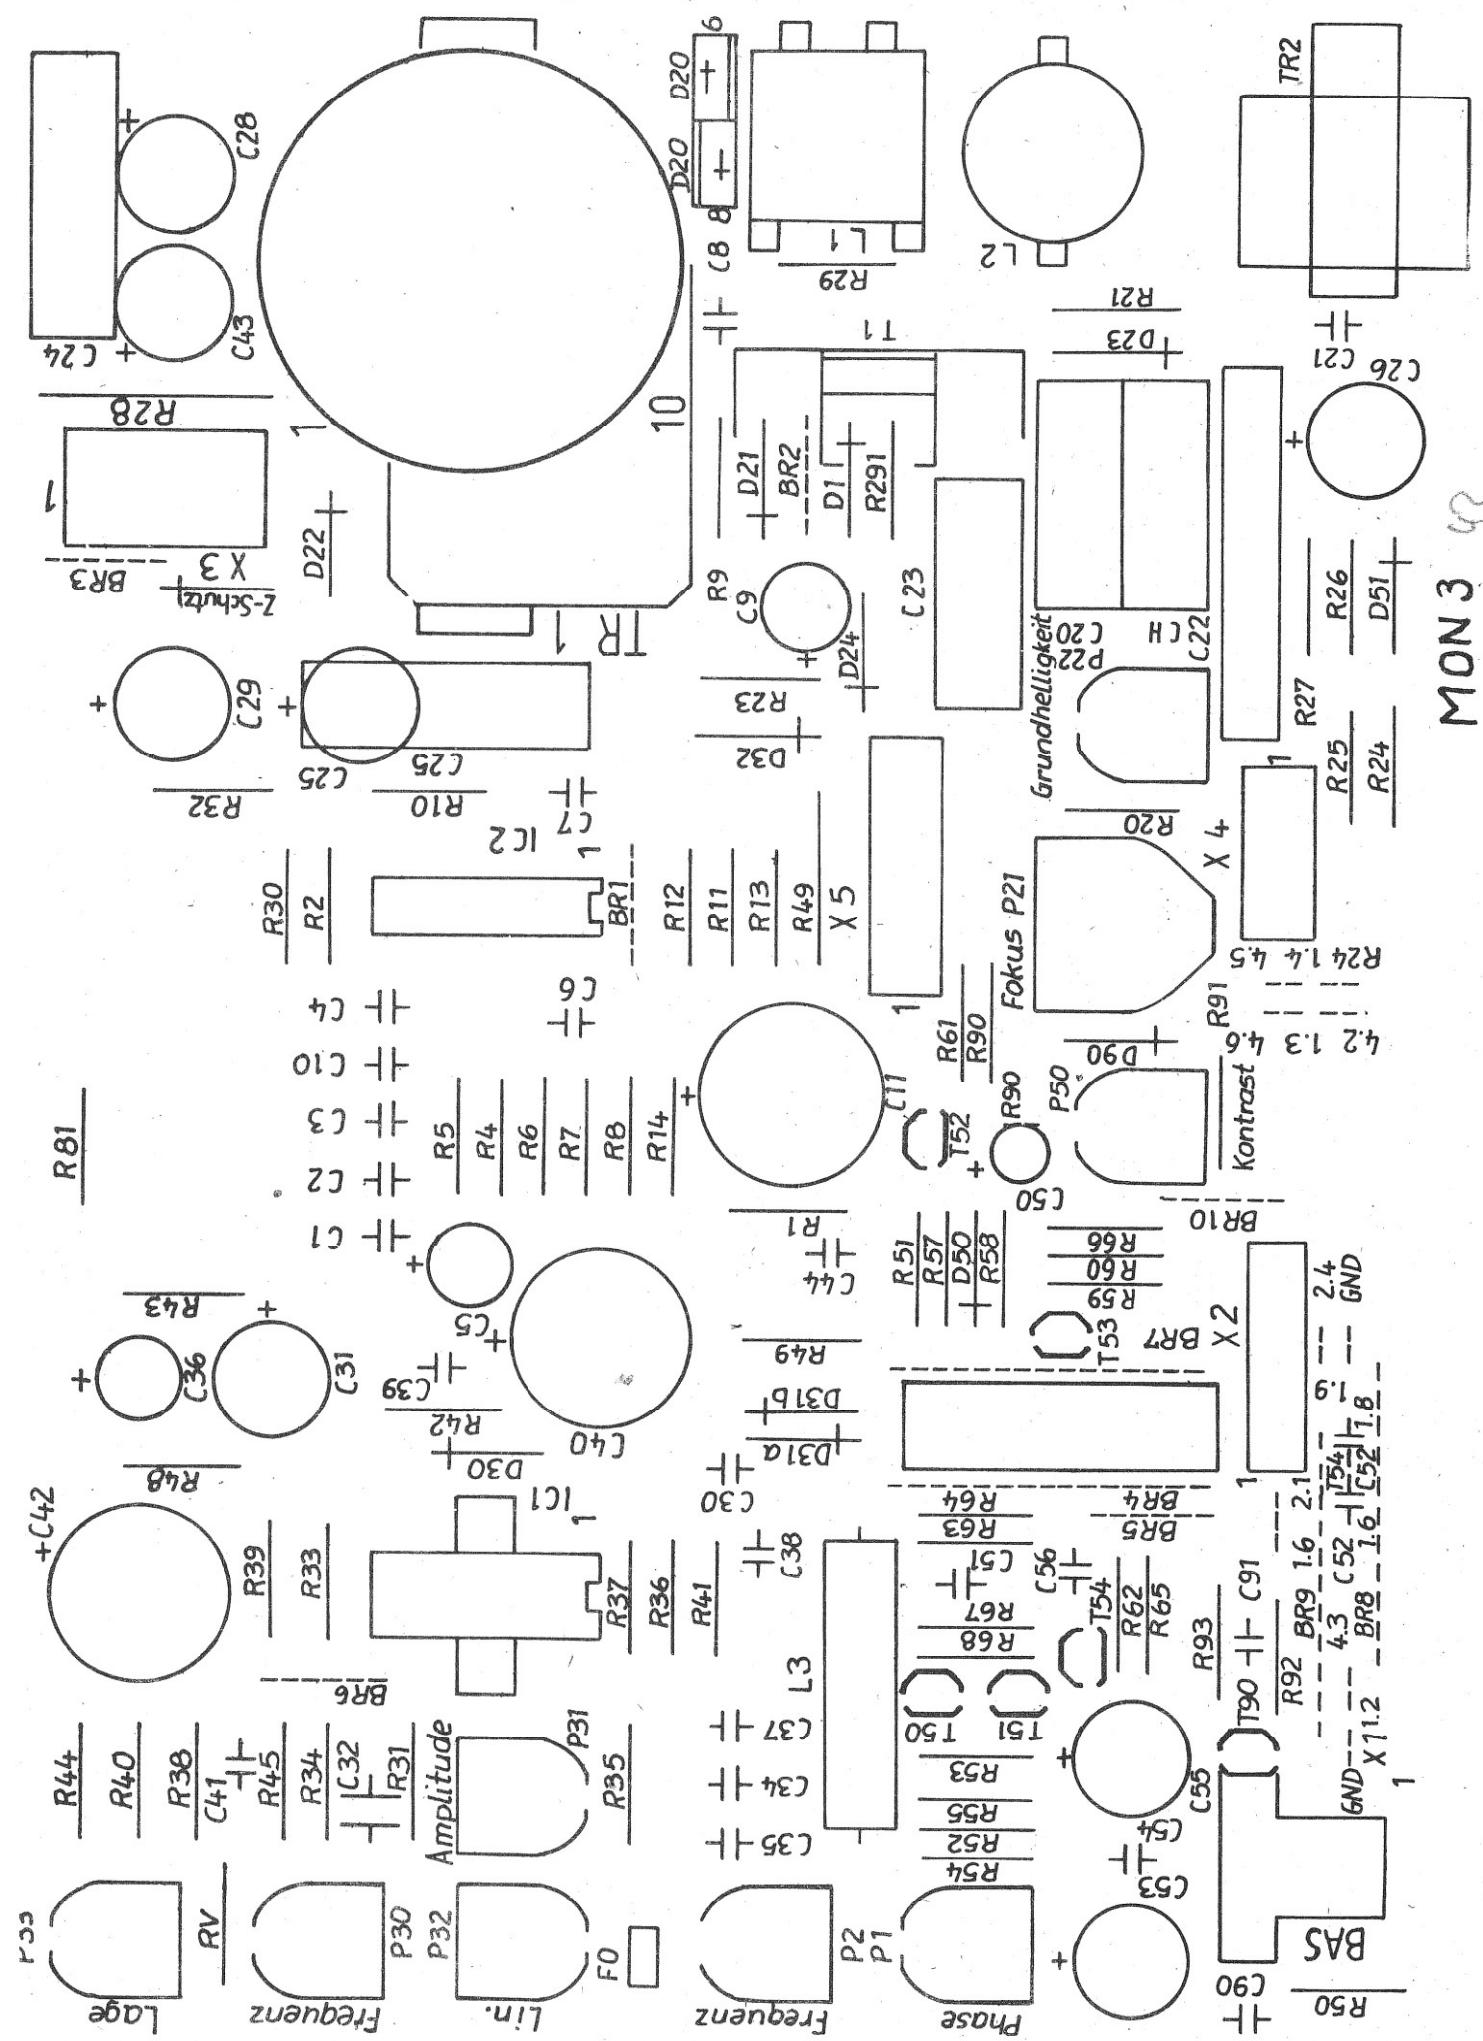

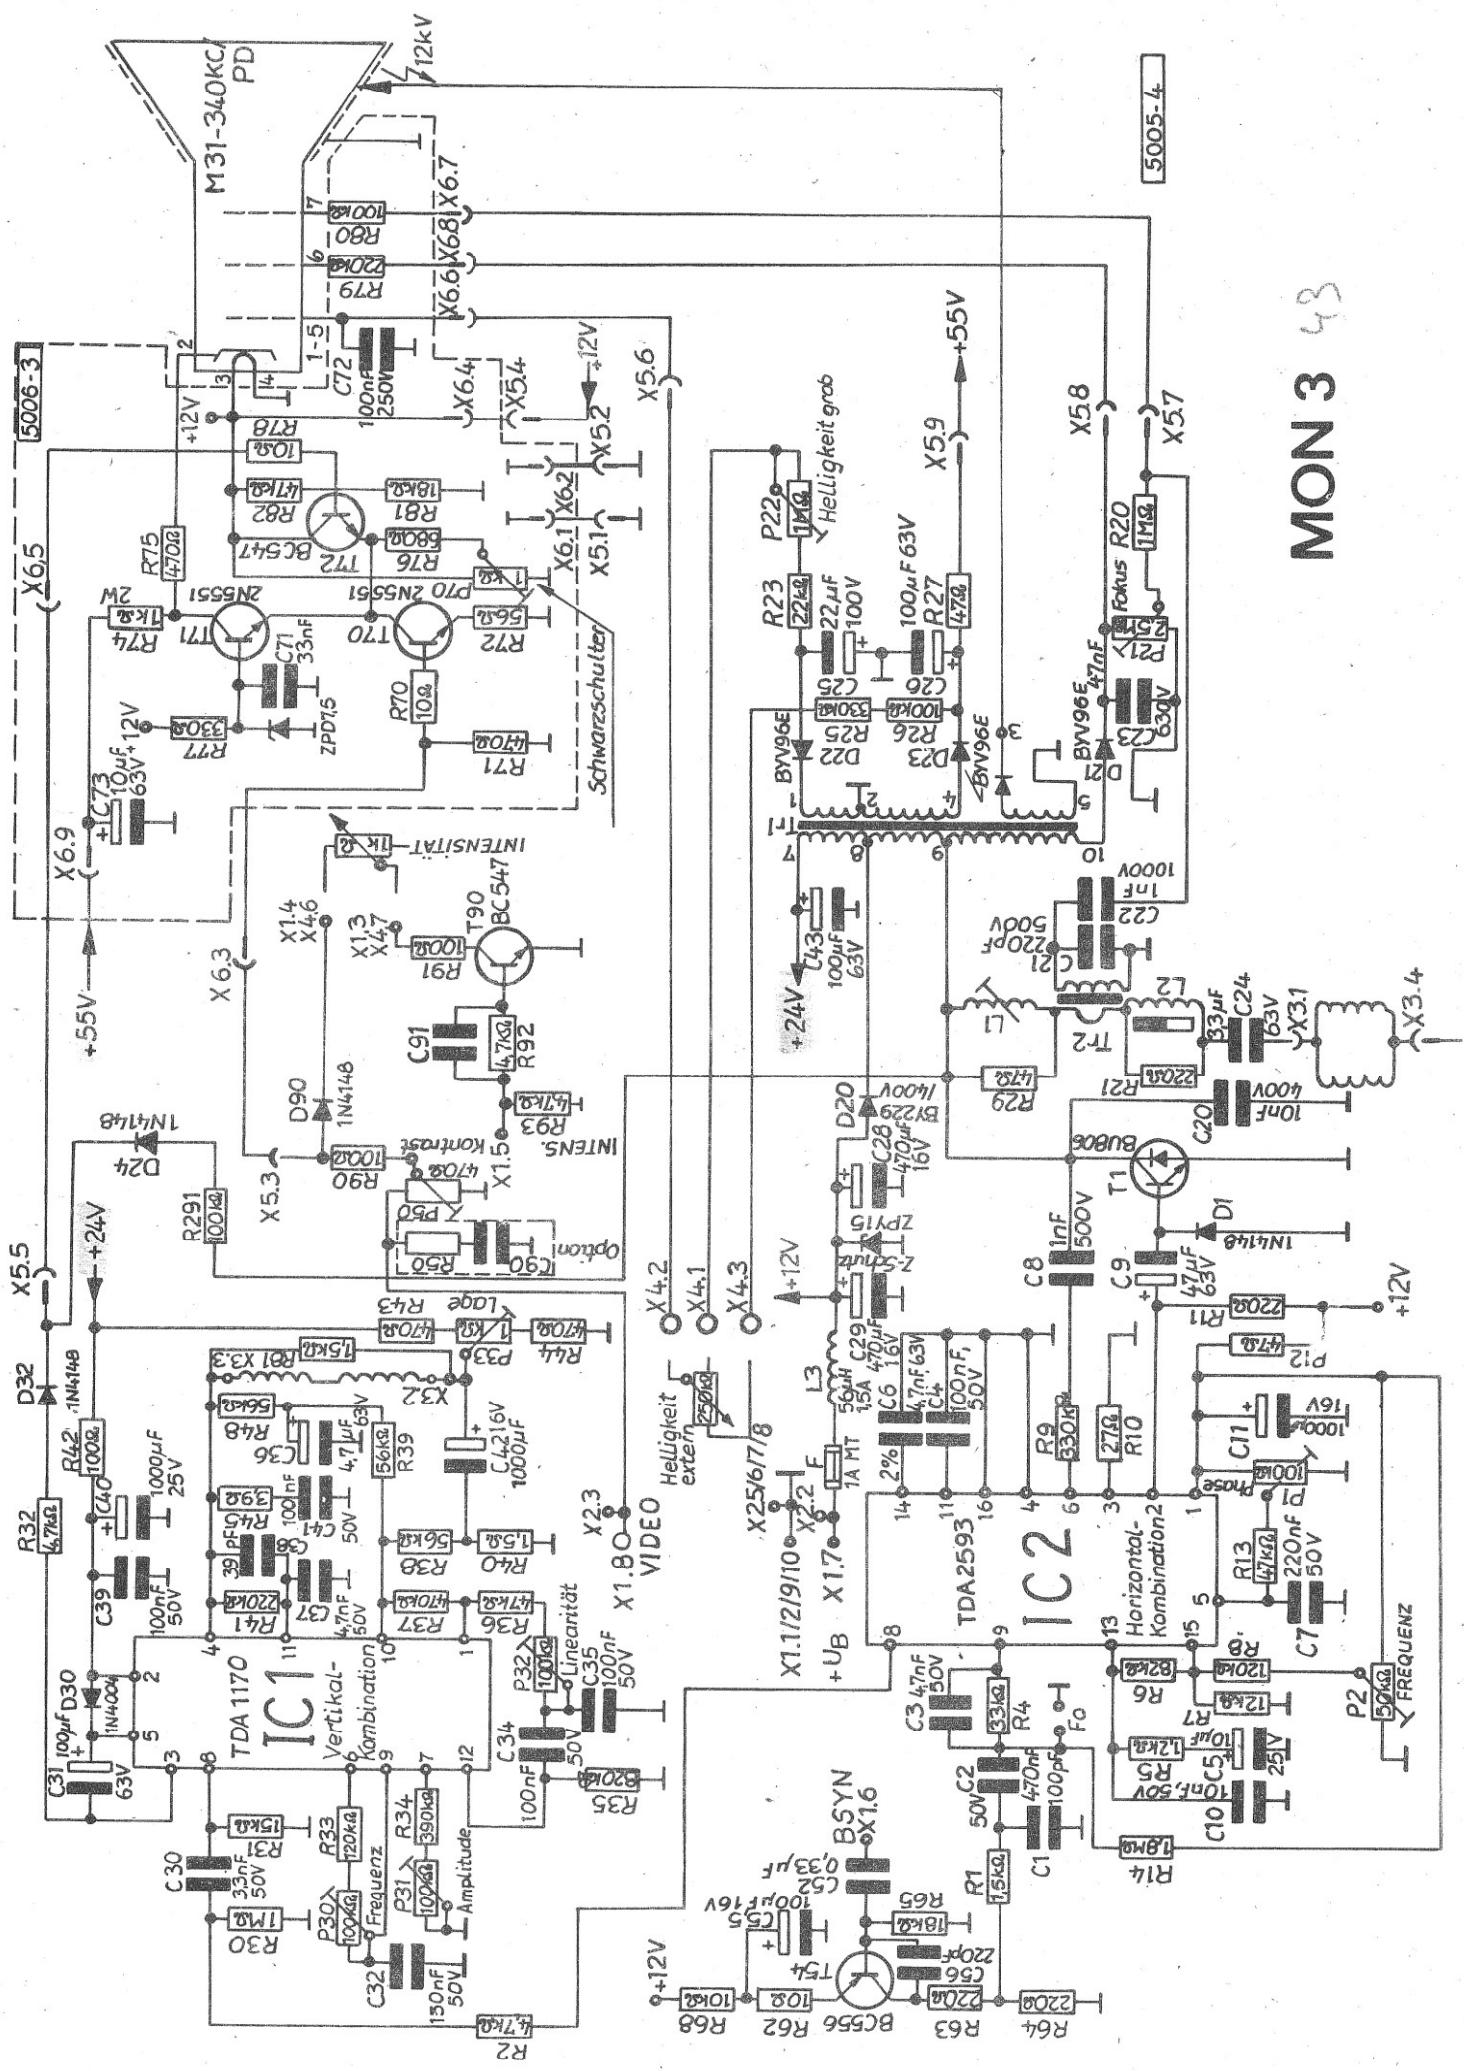

MON 3 43

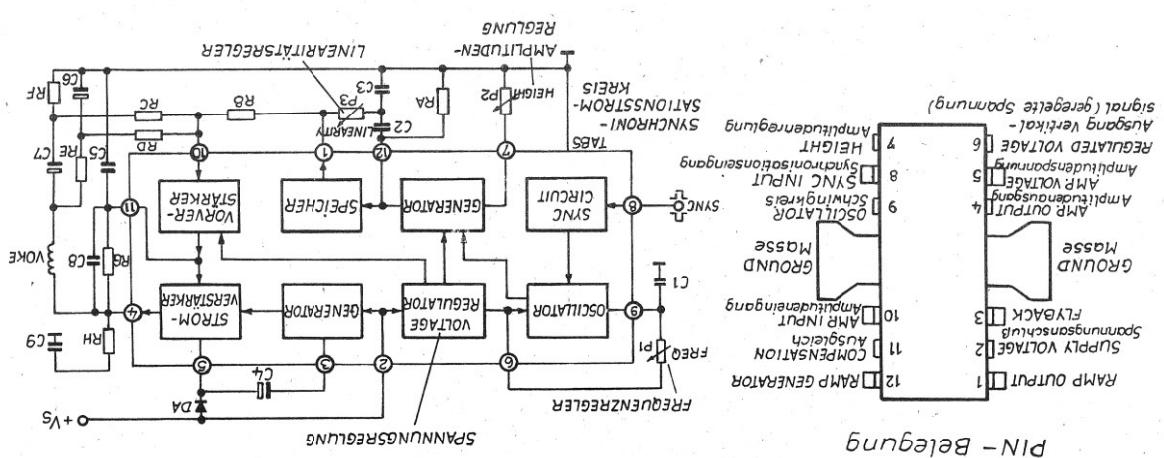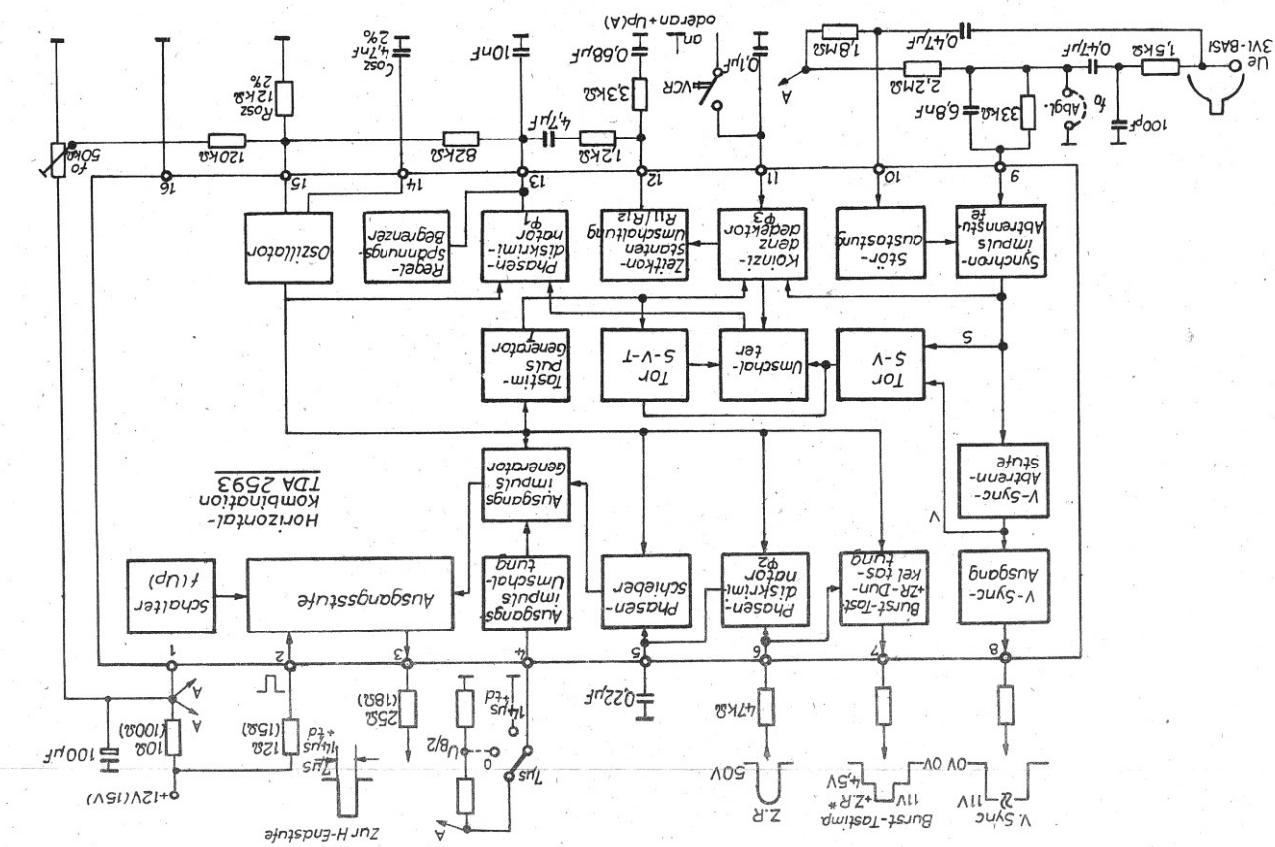

Anschub-/ und Blockdiagramm für den Schaltkreis TDA 1170 (Vertikalssteuerung) 44